

单幅立面图　1:2000

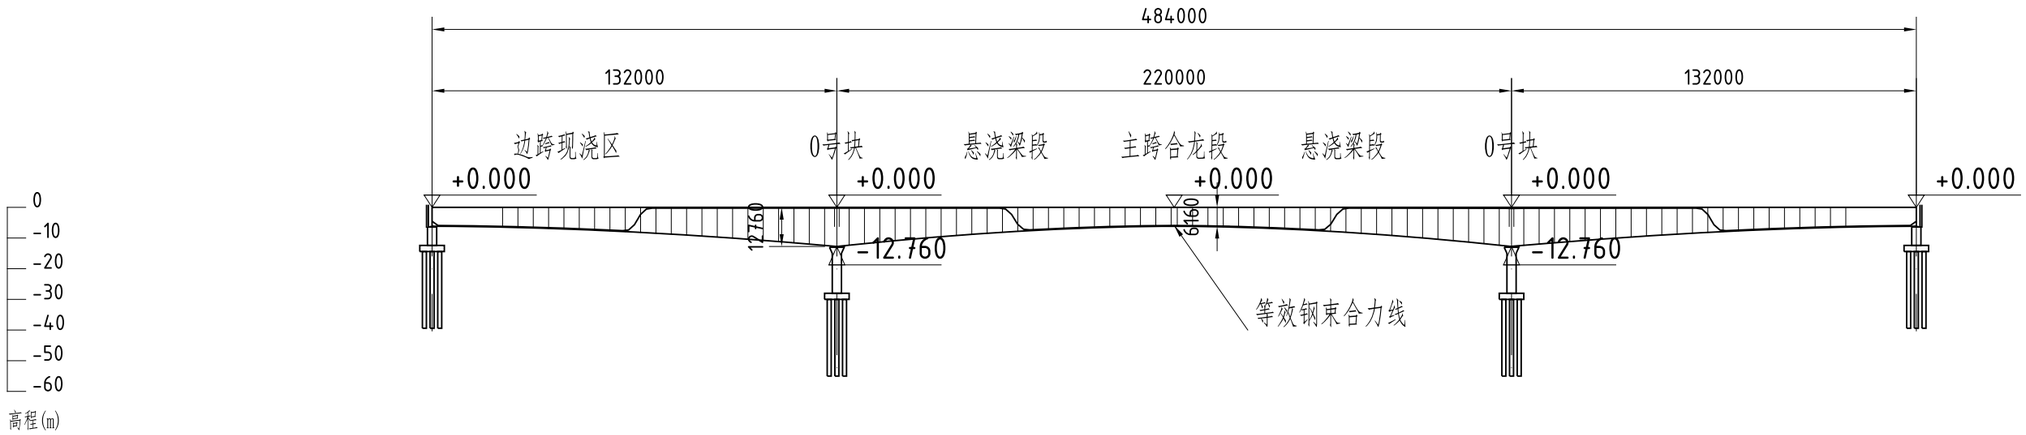

A0　　P1　　P2　　A3

K0+000.000　　K0+132.000　　K0+352.000　　K0+484.000

单幅平面图（3车道）　1:2000

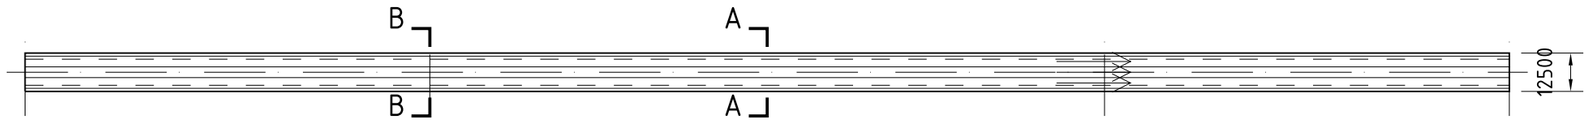

跨径组合 / m	132 + 220 + 132
单幅宽 / 全桥宽 / m	12.5 / 12.5（单幅）
跨中 / 墩顶梁高 / m	6.160 / 12.760
构造 / 混凝土	各幅单箱单室 / C50
曲线指数 / 纵坡	1.8 / 0%

相对高程：全桥中点结构顶板中心线为 0.000 m。

高程标注为梁体控制点；下部示意不代替地形或基础设计。

纵坡用于布置图；纵向计算模型仍采用水平平面梁。

注：尺寸单位mm；桩号、梁高参数单位m。

1. 3车道单幅，单箱单室。
2. 梁高、底板及腹板厚度随纵向位置变化。
3. 节段线为悬浇分段示意；施工分段应另行确定。
4. 横隔板虚线仅示位置；人孔和锚固细部另绘。
5. 下部结构及支座为示意，不表示已完成详设。
6. 仅表示已提供的等效钢束合力线，不作孔道详图。

_____		题目	三车道132+220+132m变截面连续箱梁
班级	_____	桥型总体布置图	图别　课程
姓名	软件验证示例		图号　BC-01
学号	00000000		比例　1:2000
指导老师	_____		日期　_____

校核尺100 mm（按原幅面打印）