


B-B 墩顶加厚标准截面（横隔板外侧） 1:200

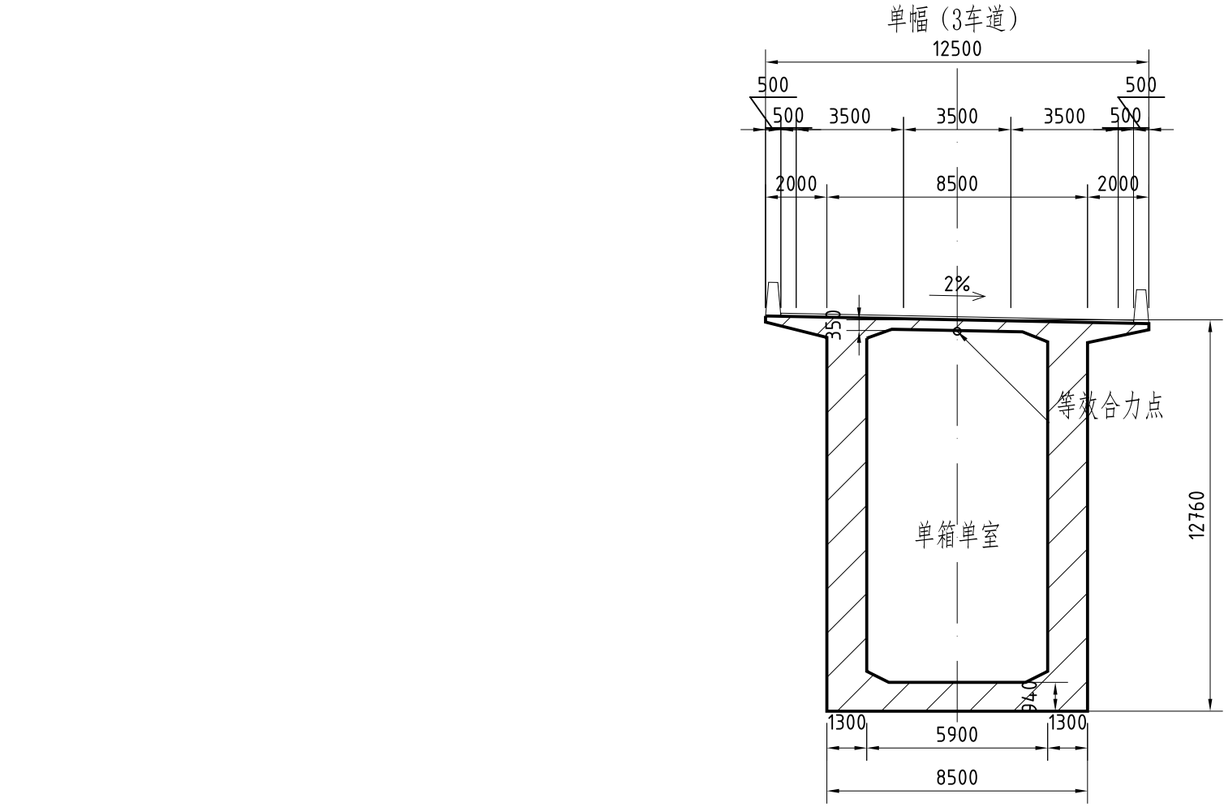

上加腋详图 1:50

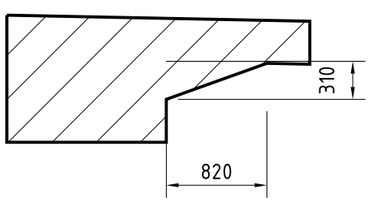

下倒角详图 1:50

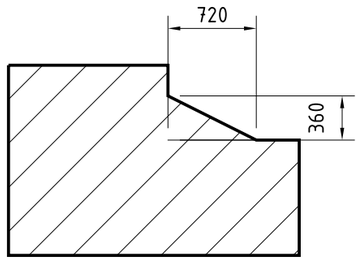

注：尺寸单位mm；定位桩号 K0+132.000。
1. 顶板厚350，底板厚940，腹板厚1300。
2. 斜线为混凝土剖切区；空腔不填充。
3. 单幅：顶板横坡2%，梁底横向水平。
4. 铺装厚100；护栏仅作外形示意。
5. 局部详图仅放大构造，几何与主断面一致。
6. 横隔板人孔、预应力锚固和钢筋详图另绘。

_____	题目	三车道132+220+132m变截面连续箱梁	
班级	_____	墩顶横断面图	图别 课程
姓名	软件验证示例		图号 BC-03
学号	00000000		比例 1:200
指导老师	_____		日期 _____

校核尺100 mm（按原幅面打印）