

## 单幅立面图 1:1000

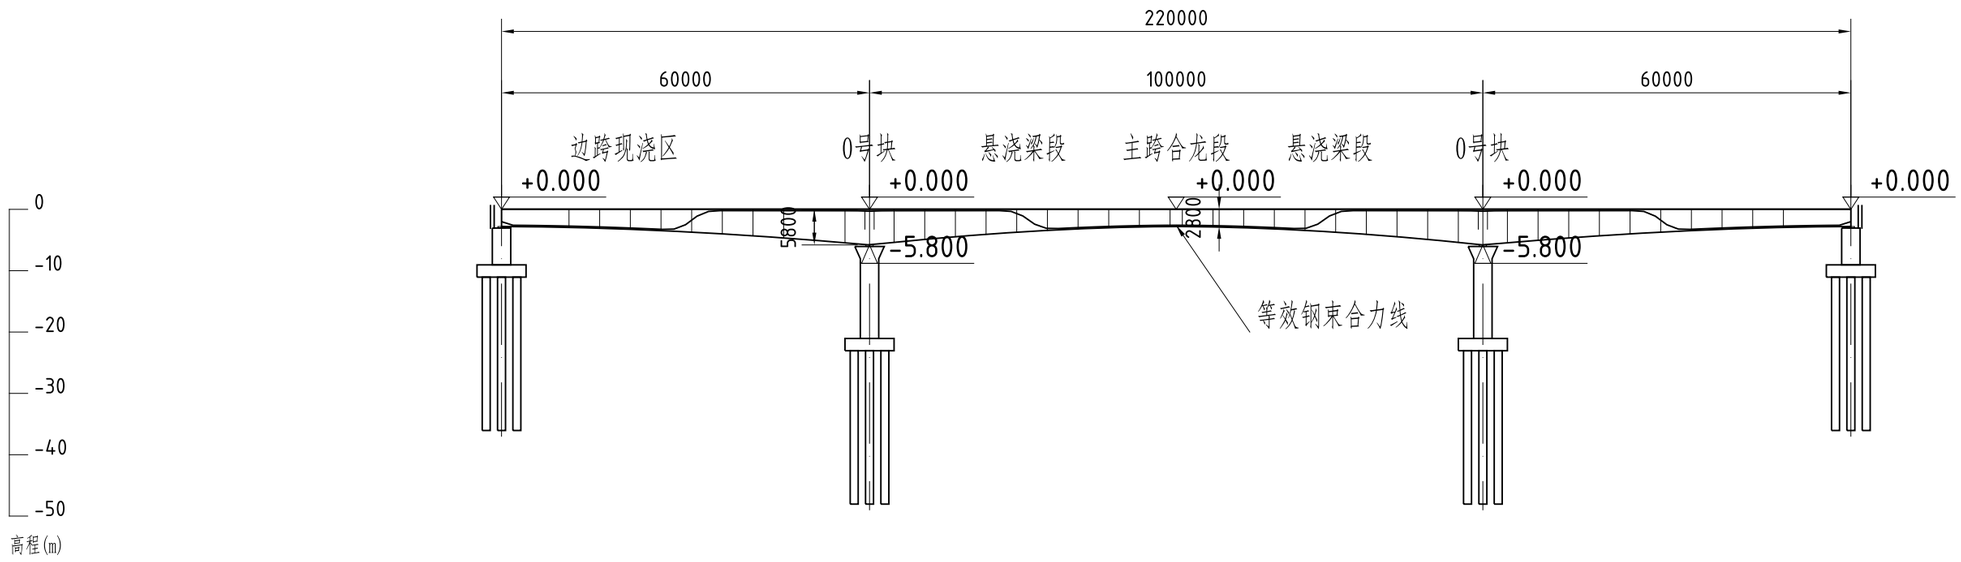


A0 K0+000.000　　P1 K0+060.000　　P2 K0+160.000　　A3 K0+220.000

## 分离式双幅平面图（每幅2车道） 1:1000

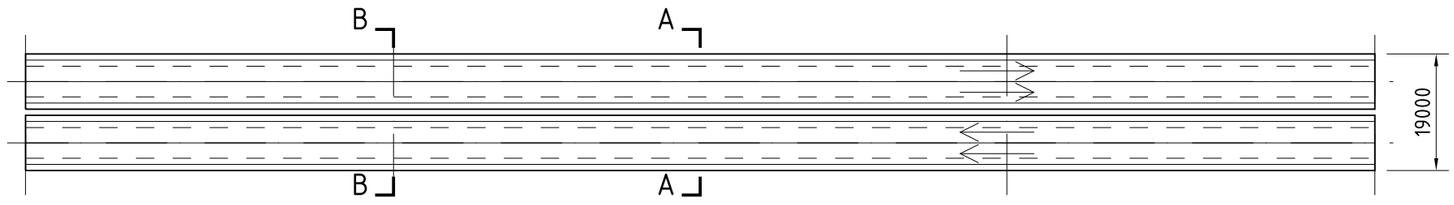


| | |
|---|---|
| 跨径组合 / m | 60 + 100 + 60 |
| 单幅宽 / 全桥宽 / m | 9 / 19（含幅间净距） |
| 跨中 / 墩顶梁高 / m | 2.800 / 5.800 |
| 构造 / 混凝土 | 各幅单箱单室 / C50 |
| 曲线指数 / 纵坡 | 1.8 / 0% |

相对高程：全桥中点结构顶板中心线为 0.000 m。

高程标注为梁体控制点；下部示意不代替地形或基础设计。

纵坡用于布置图；纵向计算模型仍采用水平平面梁。

注：尺寸单位mm；桩号、梁高参数单位m。

1. 4车道分离式，每幅2车道、单箱单室。
2. 梁高、底板及腹板厚度随纵向位置变化。
3. 节段线为悬浇分段示意；施工分段应另行确定。
4. 横隔板虚线仅示位置；人孔和锚固细部另绘。
5. 下部结构及支座为示意，不表示已完成详设。
6. 仅表示已提供的等效钢束合力线，不作孔道详图。

| | | | |
|---|---|---|---|
| _____ | | 题目 | V0.12项目展示算例 |
| 班级 | _____ | 桥型总体布置图 | 图别 / 课程 |
| 姓名 | 示例演示 | | 图号 / BC-01 |
| 学号 | 00000000 | | 比例 / 1:1000 |
| 指导老师 | _____ | | 日期 / _____ |

校核尺100 mm（按原幅面打印）