


A-A 主跨跨中标准截面　1:100

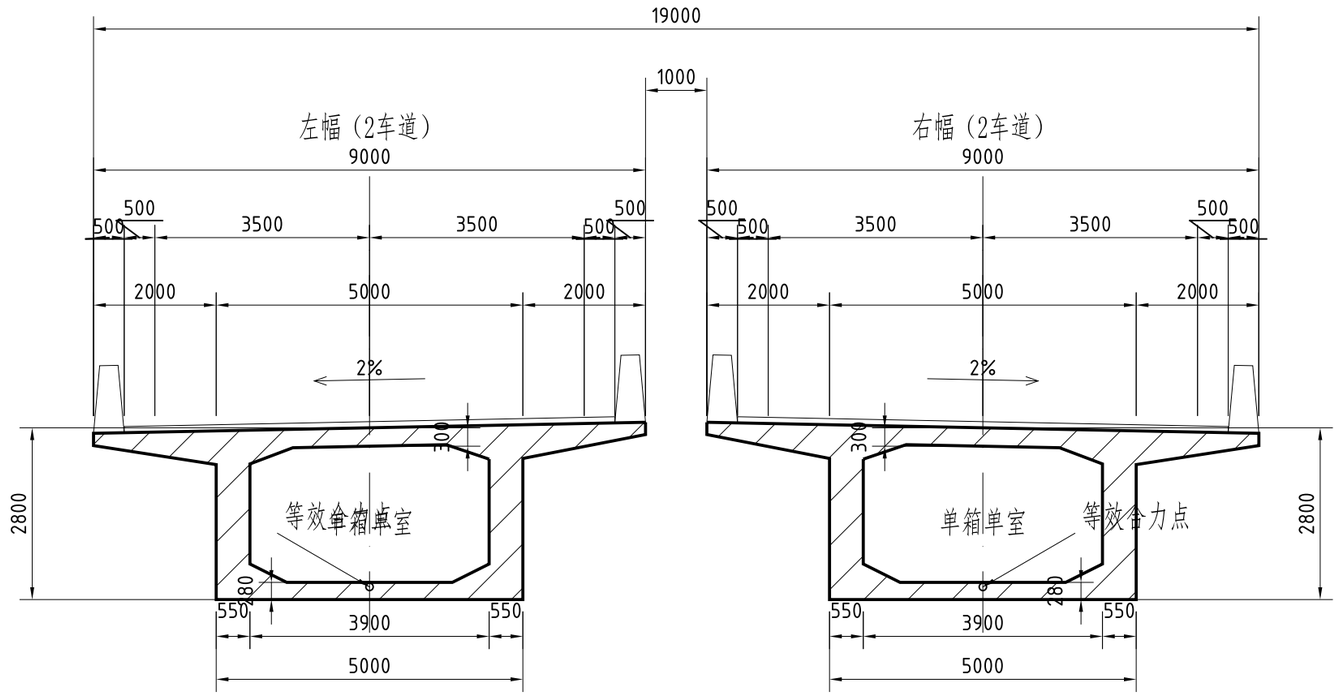

上加腋详图　1:20

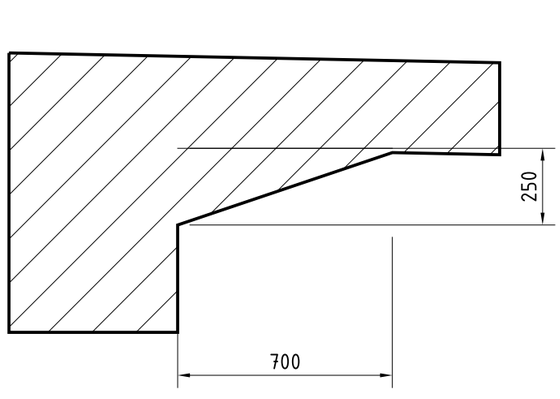

下倒角详图　1:20

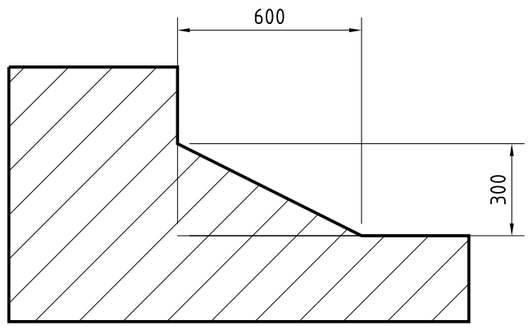

注：尺寸单位mm；定位桩号 K0+110.000。

1. 顶板厚300，底板厚280，腹板厚550。
2. 斜线为混凝土剖切区；空腔不填充。
3. 两幅镜像；顶板横坡2%，梁底横向水平。
4. 铺装厚100；护栏仅作外形示意。
5. 局部详图仅放大构造，几何与主断面一致。
6. 本图为一般构造图；不表示逐根钢筋或孔道布置。

		题目	V0.12项目展示算例		
班级	_____	跨中横断面图		图别	课程
姓名	示例演示			图号	BC-02
学号	00000000			比例	1:100
指导老师	_____			日期	_____

校核尺100 mm（按原幅面打印）