


B-B 墩顶加厚标准截面（横隔板外侧） 1:100

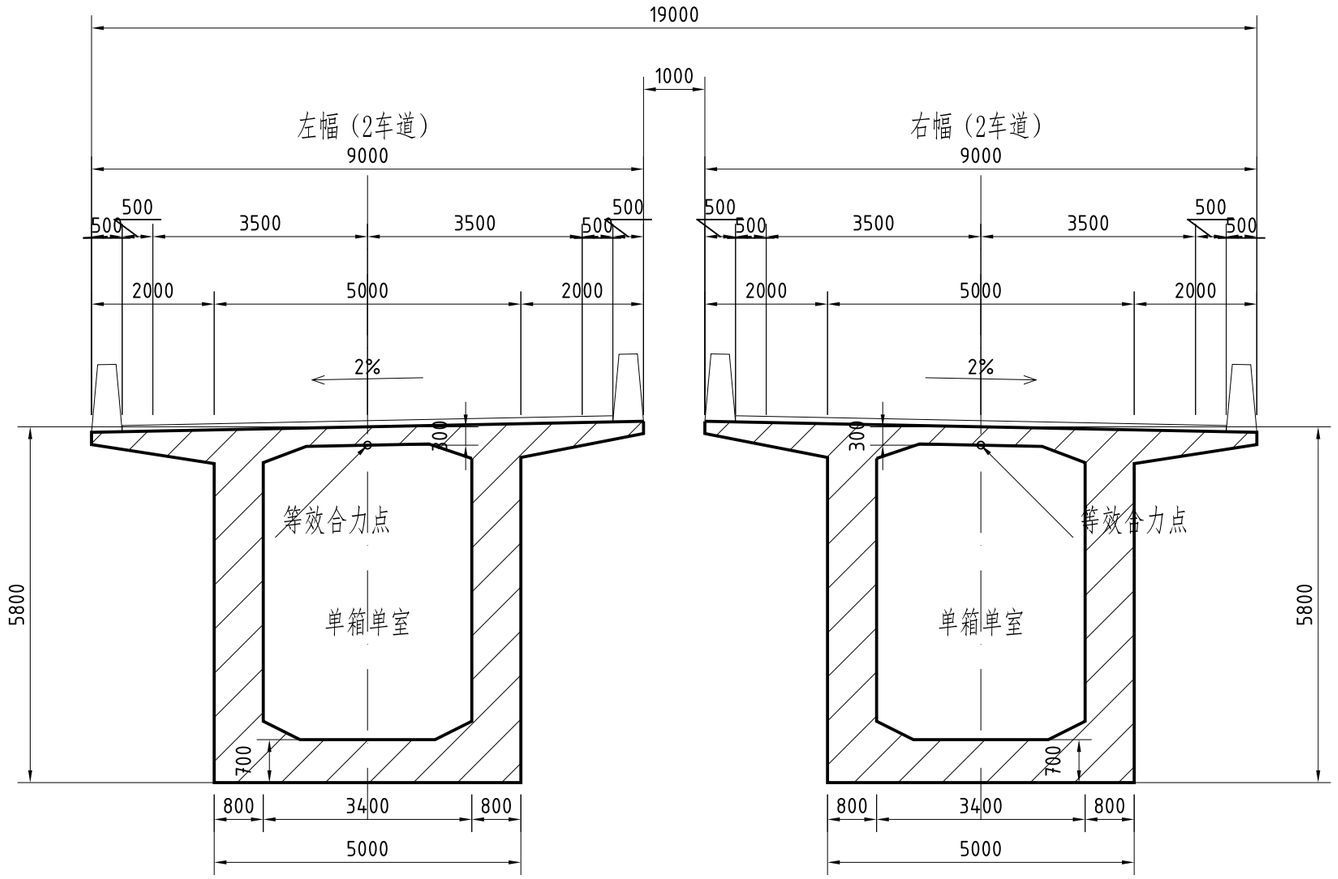

上加腋详图 1:50

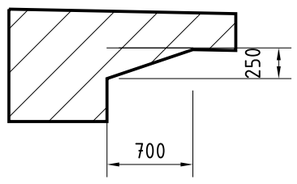

下倒角详图 1:50

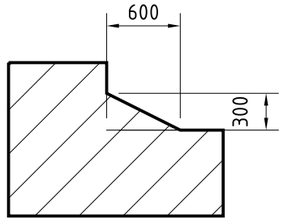

注：尺寸单位mm；定位桩号 K0+060.000。
1. 顶板厚300，底板厚700，腹板厚800。
2. 斜线为混凝土剖切区；空腔不填充。
3. 两幅镜像；顶板横坡2%，梁底横向水平。
4. 铺装厚100；护栏仅作外形示意。
5. 局部详图仅放大构造，几何与主断面一致。
6. 横隔板人孔、预应力锚固和钢筋详图另绘。

		题目	V0.12项目展示算例	
班级		墩顶横断面图	图别	课程
姓名	示例演示		图号	BC-03
学号	00000000		比例	1:100
指导老师			日期	

校核尺100 mm（按原幅面打印）